

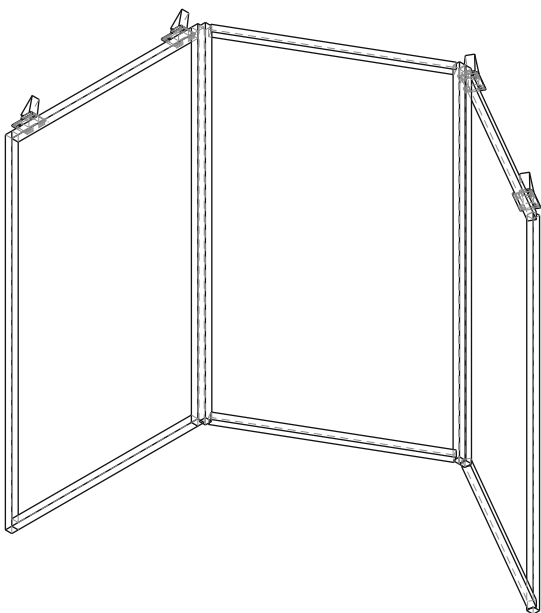
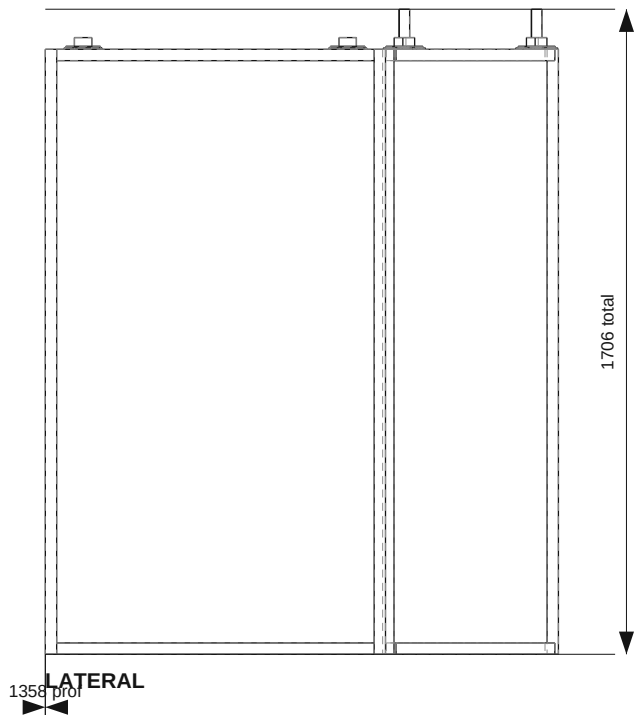


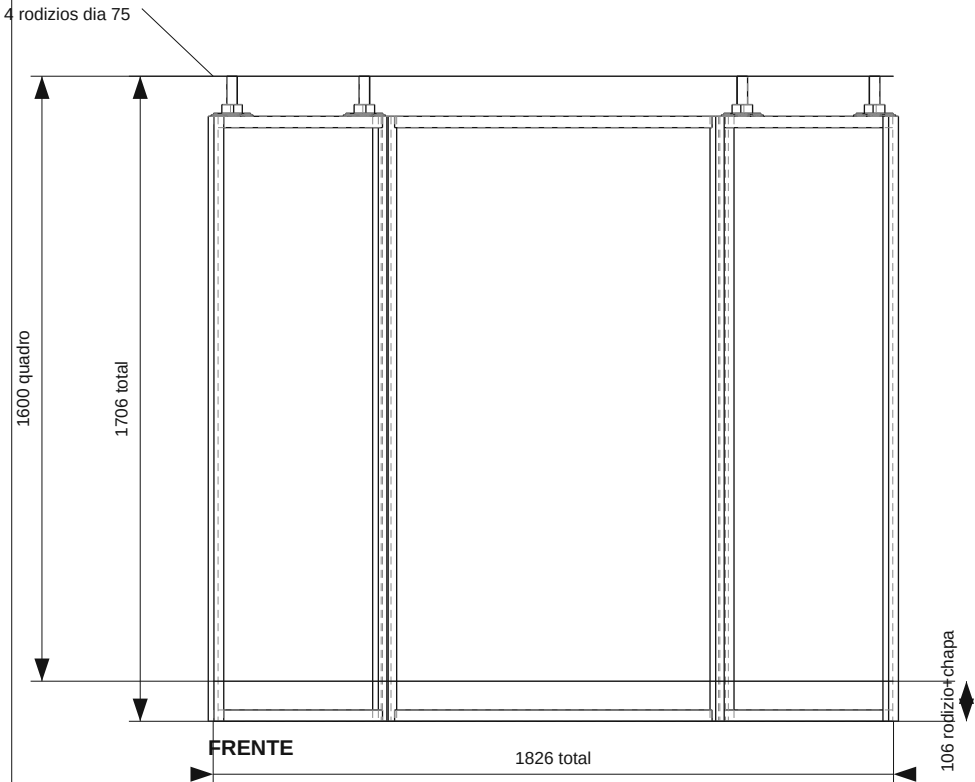

ISOMETRICA (1:25)


LISTA DE CORTE (quadro)

peca	perfil	comp.(mm)	qtd
montante	30x30x1,5	1600	6
travessa	30x30x1,5	840	6
TOTAL		14640	12
chapa base	100x70x4	100	4
rodizio	dia 75		4
2 rodizios por folha, so' nas folhas das pontas (4 un.)			

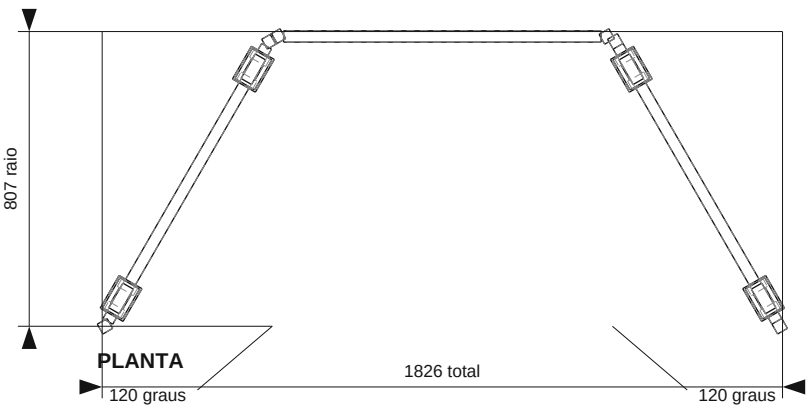

4 rasgos 25x9 passo 70x40: CONFERIR com o rodizio comprado
chapa 100x70x4 soldada sob a travessa inferior, entre o tubo e o rodizio

DETALHE BASE (1:2)

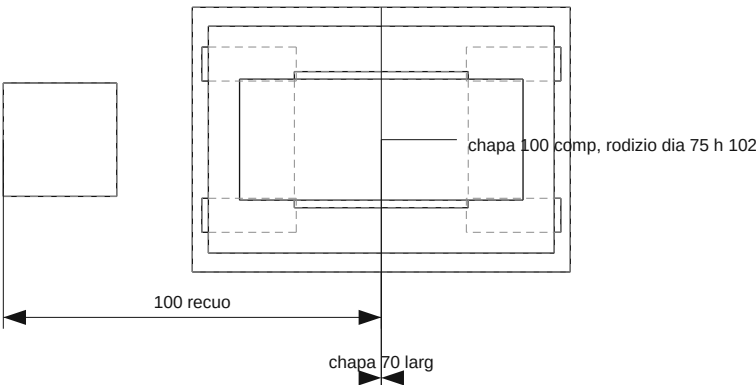

Habitat / LaRA-UERJ

BIOMBO 120 - PASSO 1B: BASE (4 RODIZIOS)

Metalon 30x30x1,5: tubo 14.64 m + 4 chapas 100x70x4 (19.65 + 0.88 kg)

FRENTE = folha central de frente; LATERAL = paralela as folhas das pontas

Escala 1:20 (detalhe 1:2) mm A3 1o diedro Rodizio dia 75 h 102 c/ freio, 4 un.

Des. A. Calvao 2026-09-18 Rev. 02